
Lácteos Altos de Teusacá · edificio de producción

Nave de 110 × 60 m · 150.000 L/día: yogures ≈ 57.000, quesos 50.000 y leche UHT 43.000 L/día · códigos ISA-88 de las recetas, el P&ID y el ISA-95 · paletizado manual

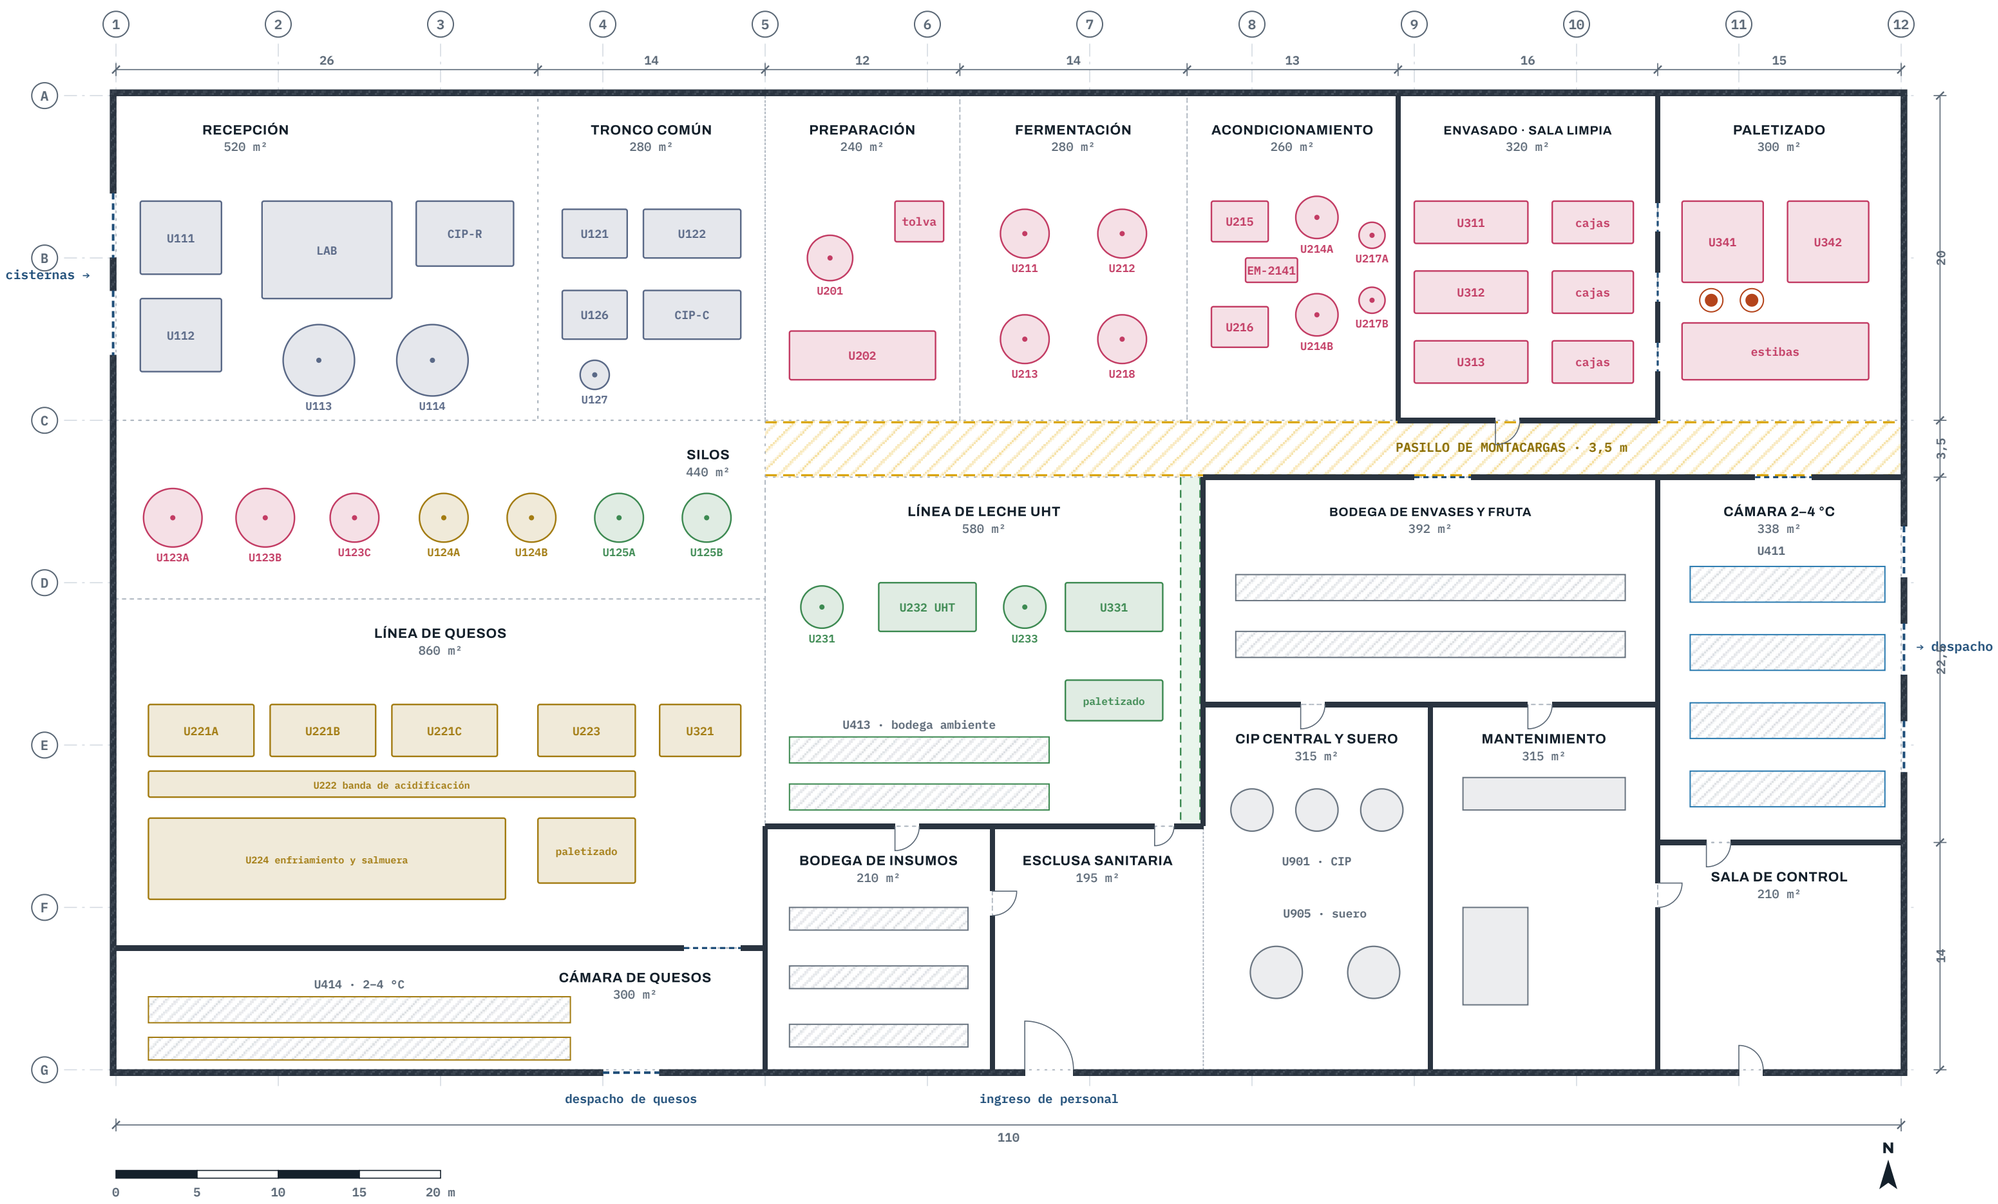

Convenciones

- Muro exterior (30 cm)
- Muro interior y puerta con su giro
- Portón, o paso de banda en un muro
- Límite de área sin muro (nave abierta)
- Pasillo de montacargas (3,5 m)
- Pasillo peatonal (1,2 m)
- Piso libre
- Tronco común
- Línea de yogures
- Línea de quesos
- Línea de leche UHT
- Servicios y almacén
- Estanterías
- Operario de paletizado manual

Áreas y espacio libre

Recinto	m²	libre
Recepción	520	72 %
Tronco común	280	78 %
Silos	440	87 %
Preparación	240	83 %
Fermentación	280	90 %
Acondicionamiento	260	86 %
Envasado · sala limpia	320	71 %
Paletizado	300	70 %
Línea de quesos	860	67 %
Cámara de quesos	300	74 %
Línea de leche UHT	580	81 %
Bodega de envases y fruta	392	80 %
Cámara 2–4 °C	338	69 %
Bodega de insumos	210	78 %
Esclusa sanitaria	195	100 %
CIP central y suero	315	90 %
Mantenimiento	315	86 %
Sala de control	210	100 %
Total	**6.355**	**79 %**

Libre = área del recinto sin equipos ni estanterías; incluye las zonas de operación y mantenimiento.

PROYECTO
Proyecto integrador APM 2026-2S · UNAL

PLANO
Distribución en planta · tres líneas

ESCALA
1:750 en A3 · cotas en m

FECHA
11-oct-2026

Mekvra · medidas propuestas, sin plano del terreno