


Línea de yogures · paletizado manual

La línea de yogures en color y las demás áreas en gris · en U341 dos operarios estiban a mano las cajas que llegan por las bandas

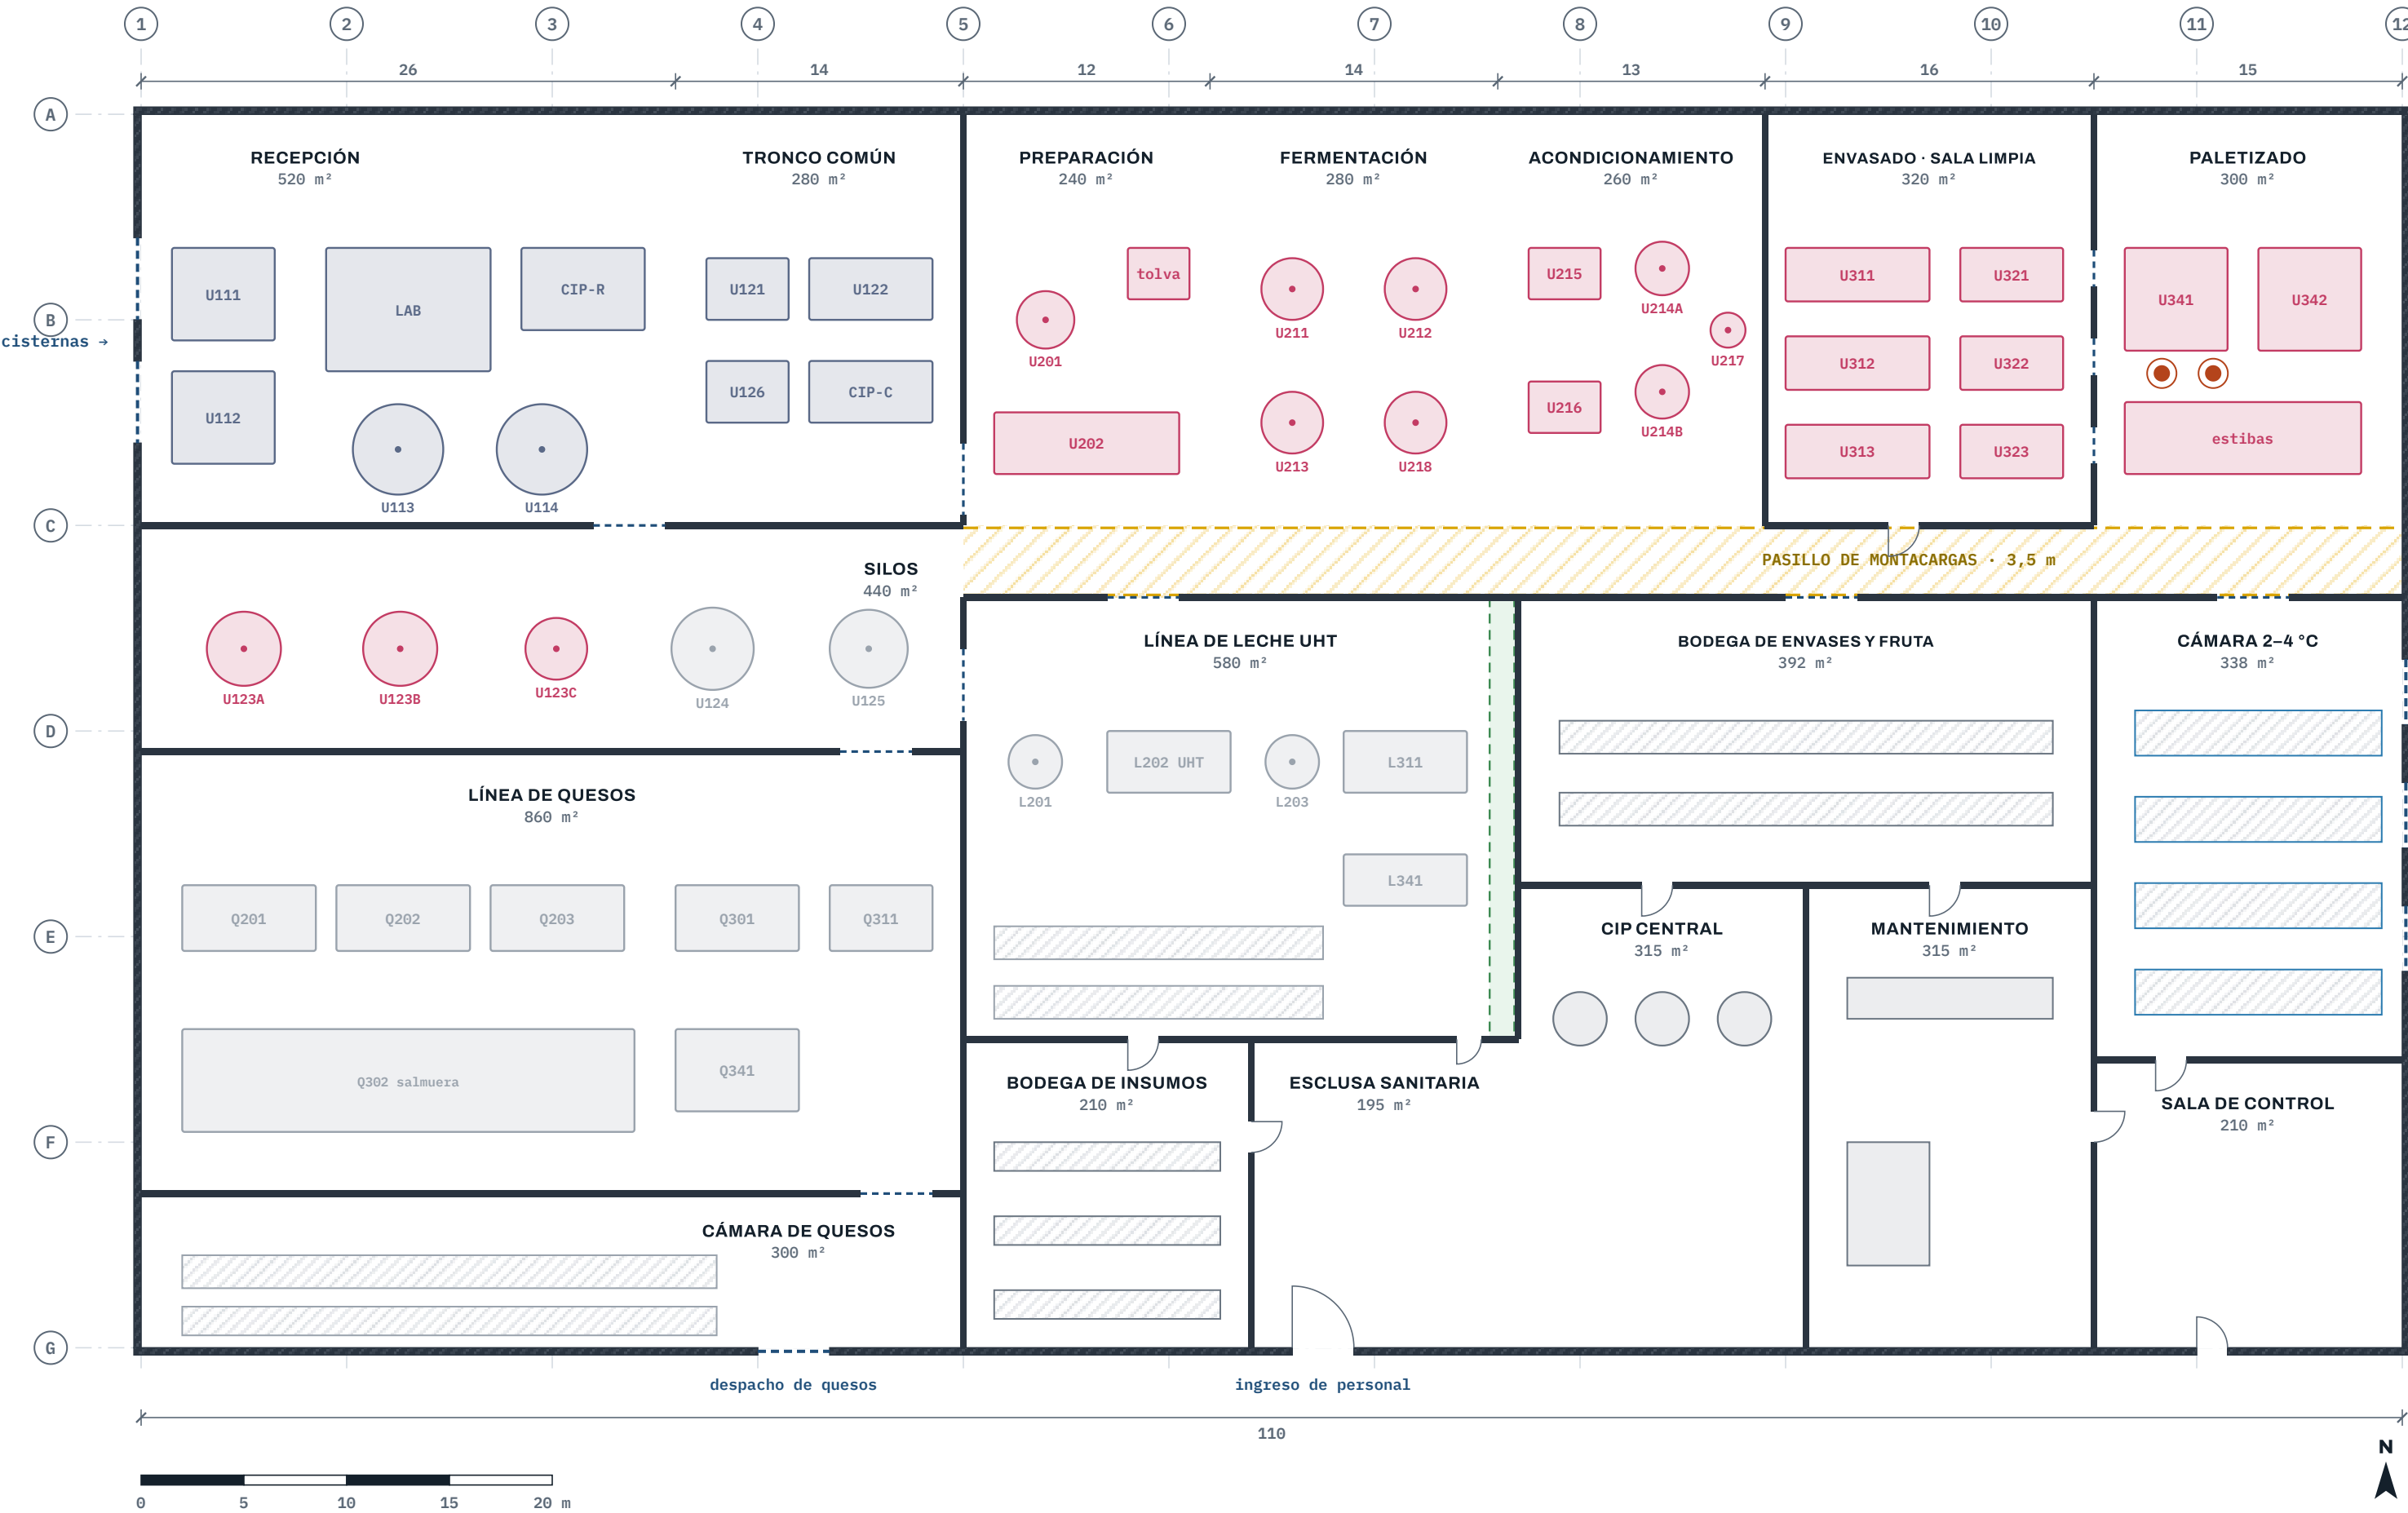

Convenciones

- Muro exterior (30 cm)
- Muro interior y puerta con su giro
- Portón, o paso de banda en un muro
- Pasillo de montacargas (3,5 m)
- Pasillo peatonal (1,2 m)
- Piso libre
- Tronco común
- Línea de yogures
- Línea de quesos (otra línea)
- Línea de leche UHT (otra línea)
- Servicios y almacén
- Estanterías
- Operario de paletizado manual

Áreas y espacio libre

Recinto	m²	libre
Siilos	440	88 %
Preparación	240	83 %
Fermentación	280	90 %
Acondicionamiento	260	88 %
Envasado · sala limpia	320	71 %
Paletizado	300	70 %
Bodega de envases y fruta	392	80 %
Cámara 2-4 °C	338	69 %
Bodega de insumos	210	78 %
Total	2.780	80 %

Libre = área del recinto sin equipos ni estanterías; incluye las zonas de operación y mantenimiento.

PROYECTO
Proyecto integrador APM 2026-2S · UNAL

PLANO
Distribución · línea de yogures

ESCALA
1:750 en A3 · cotas en m

FECHA
10-oct-2026

Mekvra · medidas propuestas, sin plano del terreno