


# Lácteos Altos de Teusacá · edificio de producción

Nave de 110 × 60 m · 150.000 L/día: yogures ≈ 57.000, quesos 50.000 y leche UHT 43.000 L/día · códigos de equipo iguales a los del modelo de Tecnomatix

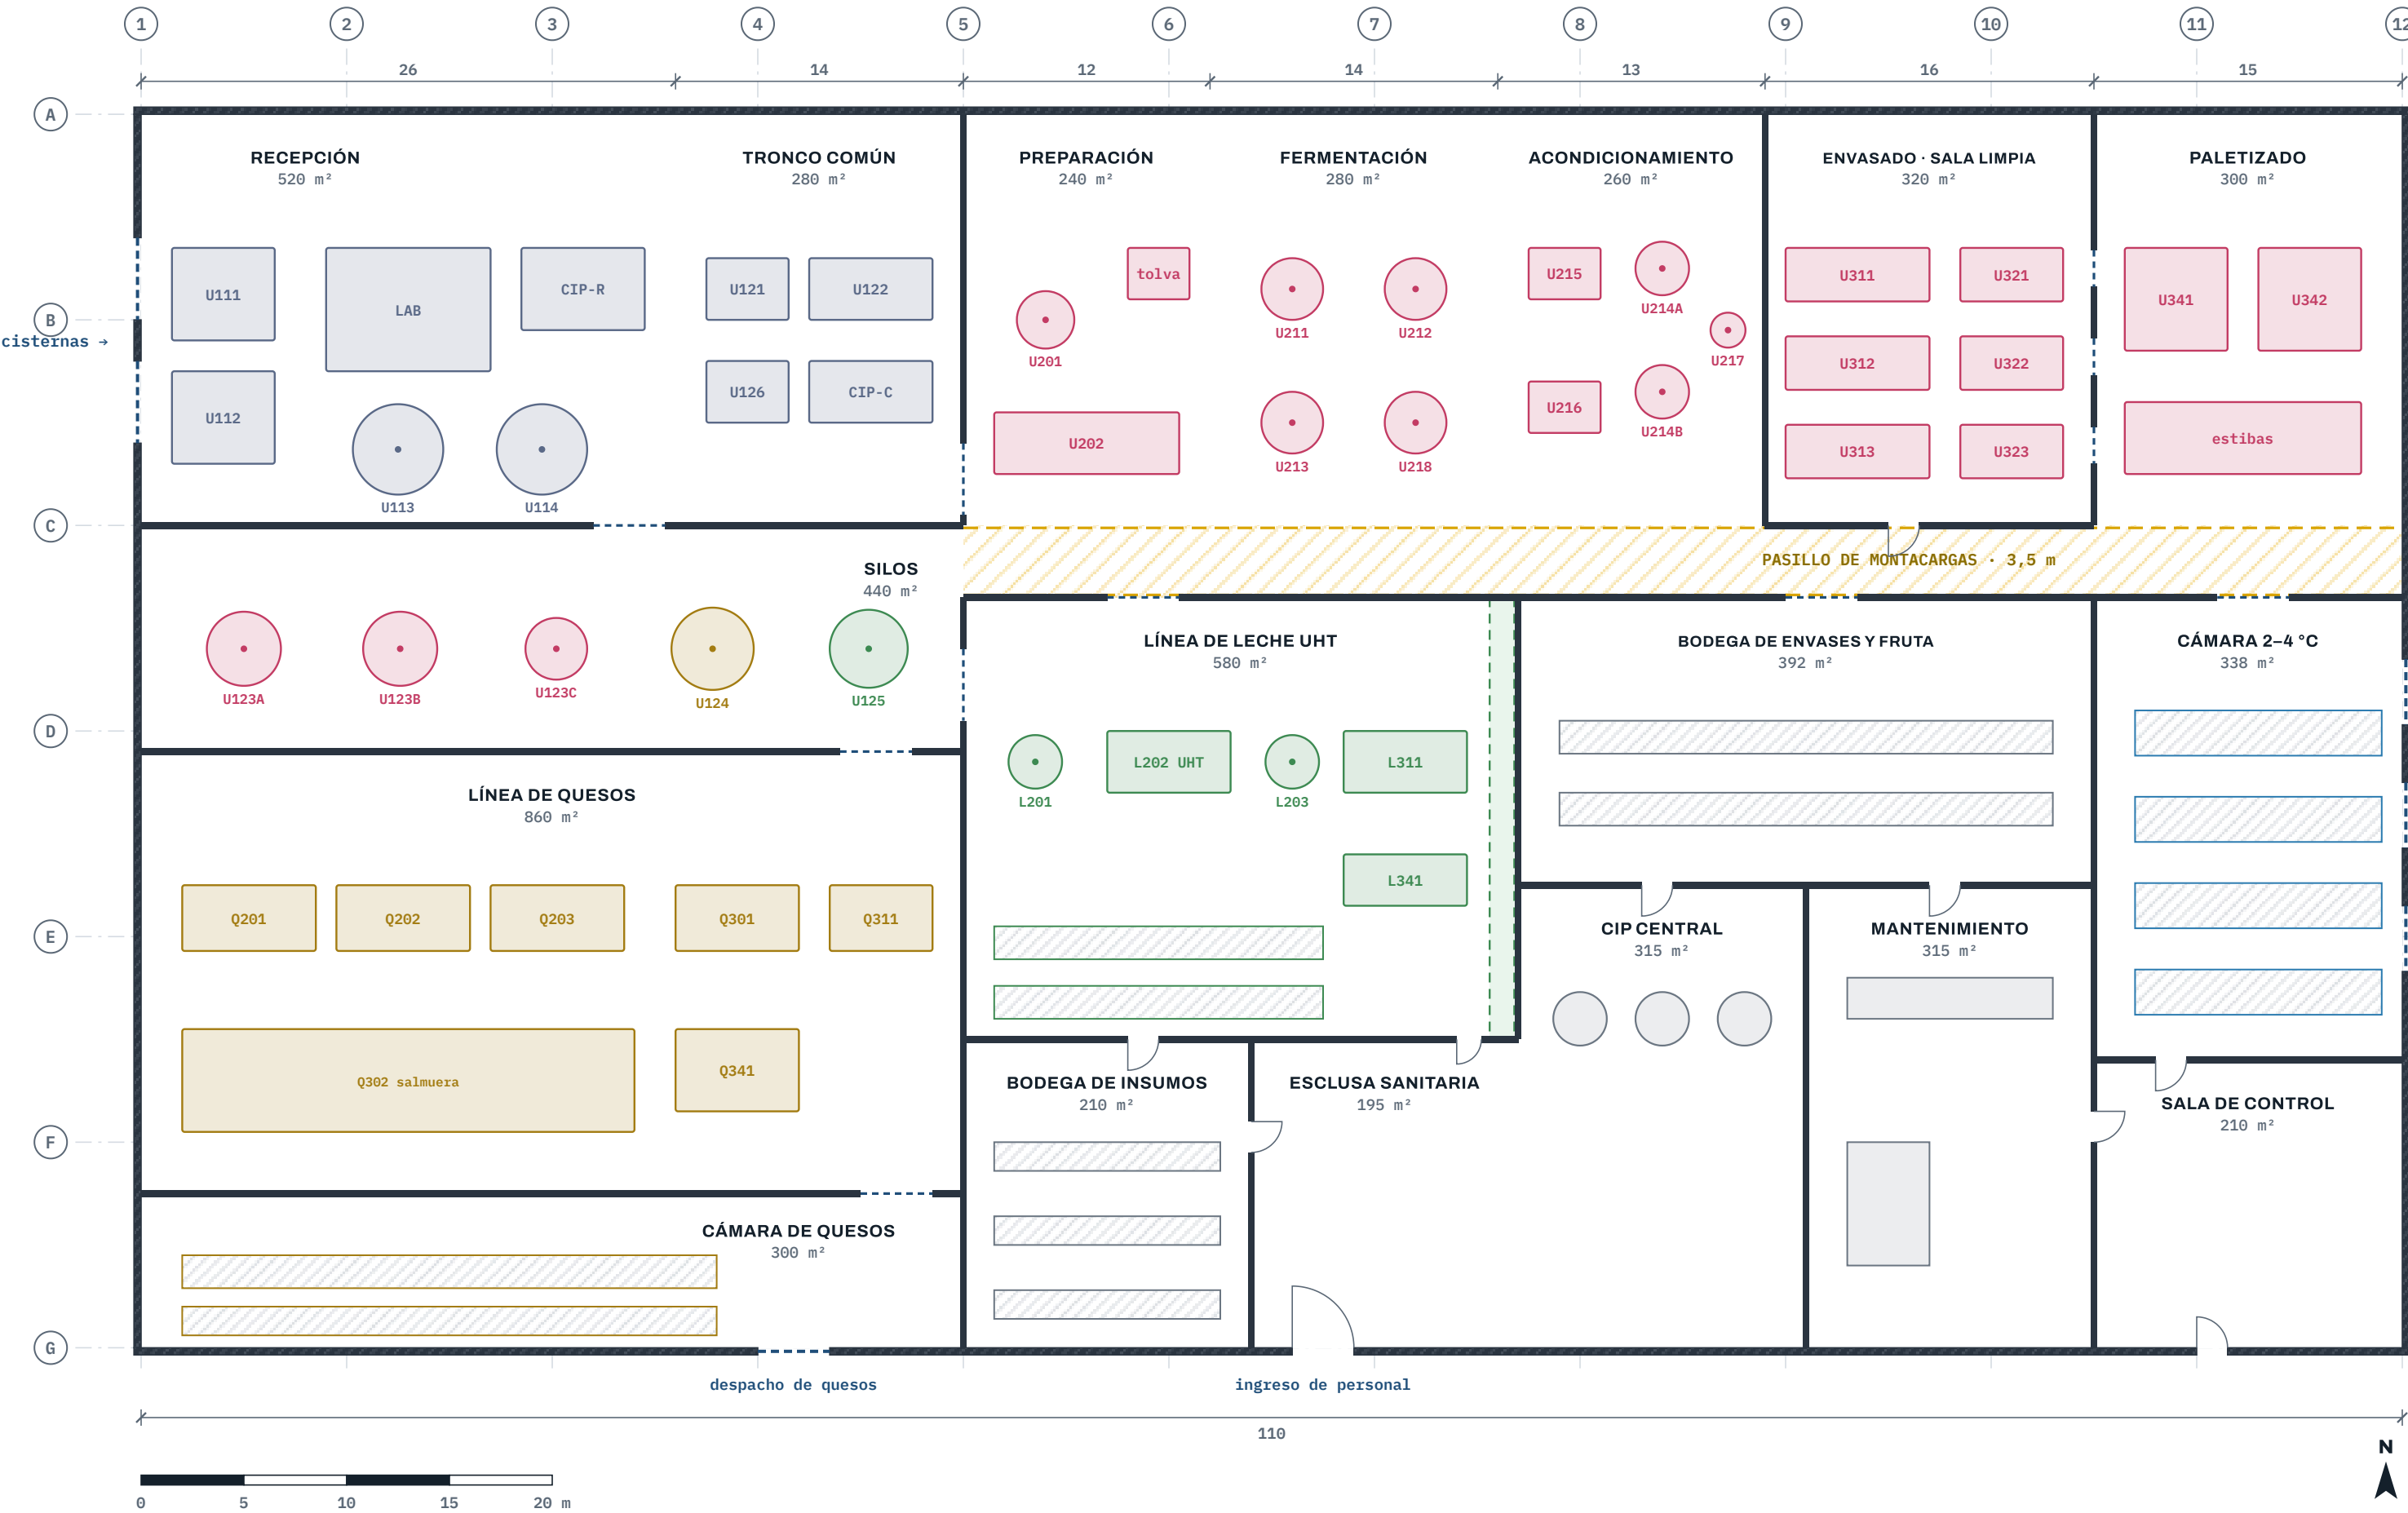

## Convenciones

- Muro exterior (30 cm)
- Muro interior y puerta con su giro
- Portón, o paso de banda en un muro
- Pasillo de montacargas (3,5 m)
- Pasillo peatonal (1,2 m)
- Piso libre
- Tronco común
- Línea de yogures
- Línea de quesos
- Línea de leche UHT
- Servicios y almacén
- Estanterías

## Áreas y espacio libre

| Recinto                   | m²           | libre       |
|---------------------------|--------------|-------------|
| Recepción                 | 520          | 72 %        |
| Tronco común              | 280          | 79 %        |
| Silos                     | 440          | 88 %        |
| Preparación               | 240          | 83 %        |
| Fermentación              | 280          | 90 %        |
| Acondicionamiento         | 260          | 88 %        |
| Envasado · sala limpia    | 320          | 71 %        |
| Paletizado                | 300          | 70 %        |
| Línea de quesos           | 860          | 73 %        |
| Cámara de quesos          | 300          | 74 %        |
| Línea de leche UHT        | 580          | 81 %        |
| Bodega de envases y fruta | 392          | 80 %        |
| Cámara 2-4 °C             | 338          | 69 %        |
| Bodega de insumos         | 210          | 78 %        |
| Esclusa sanitaria         | 195          | 100 %       |
| CIP central               | 315          | 95 %        |
| Mantenimiento             | 315          | 86 %        |
| Sala de control           | 210          | 100 %       |
| <b>Total</b>              | <b>6.355</b> | <b>80 %</b> |

Libre = área del recinto sin equipos ni estanterías; incluye las zonas de operación y mantenimiento.

PROYECTO  
Proyecto integrador APM 2026-2S · UNAL

PLANO  
Distribución en planta · tres líneas

ESCALA  
1:750 en A3 · cotas en m

FECHA  
10-oct-2026

Mekvra · medidas propuestas, sin plano del terreno