


Lácteos Altos de Teusacá • planta de 150.000 L/día

Yogures ≈ 57.000 L/día • quesos 50.000 L/día • leche UHT 43.000 L/día • códigos de equipo iguales a los del modelo de Tecnomatix

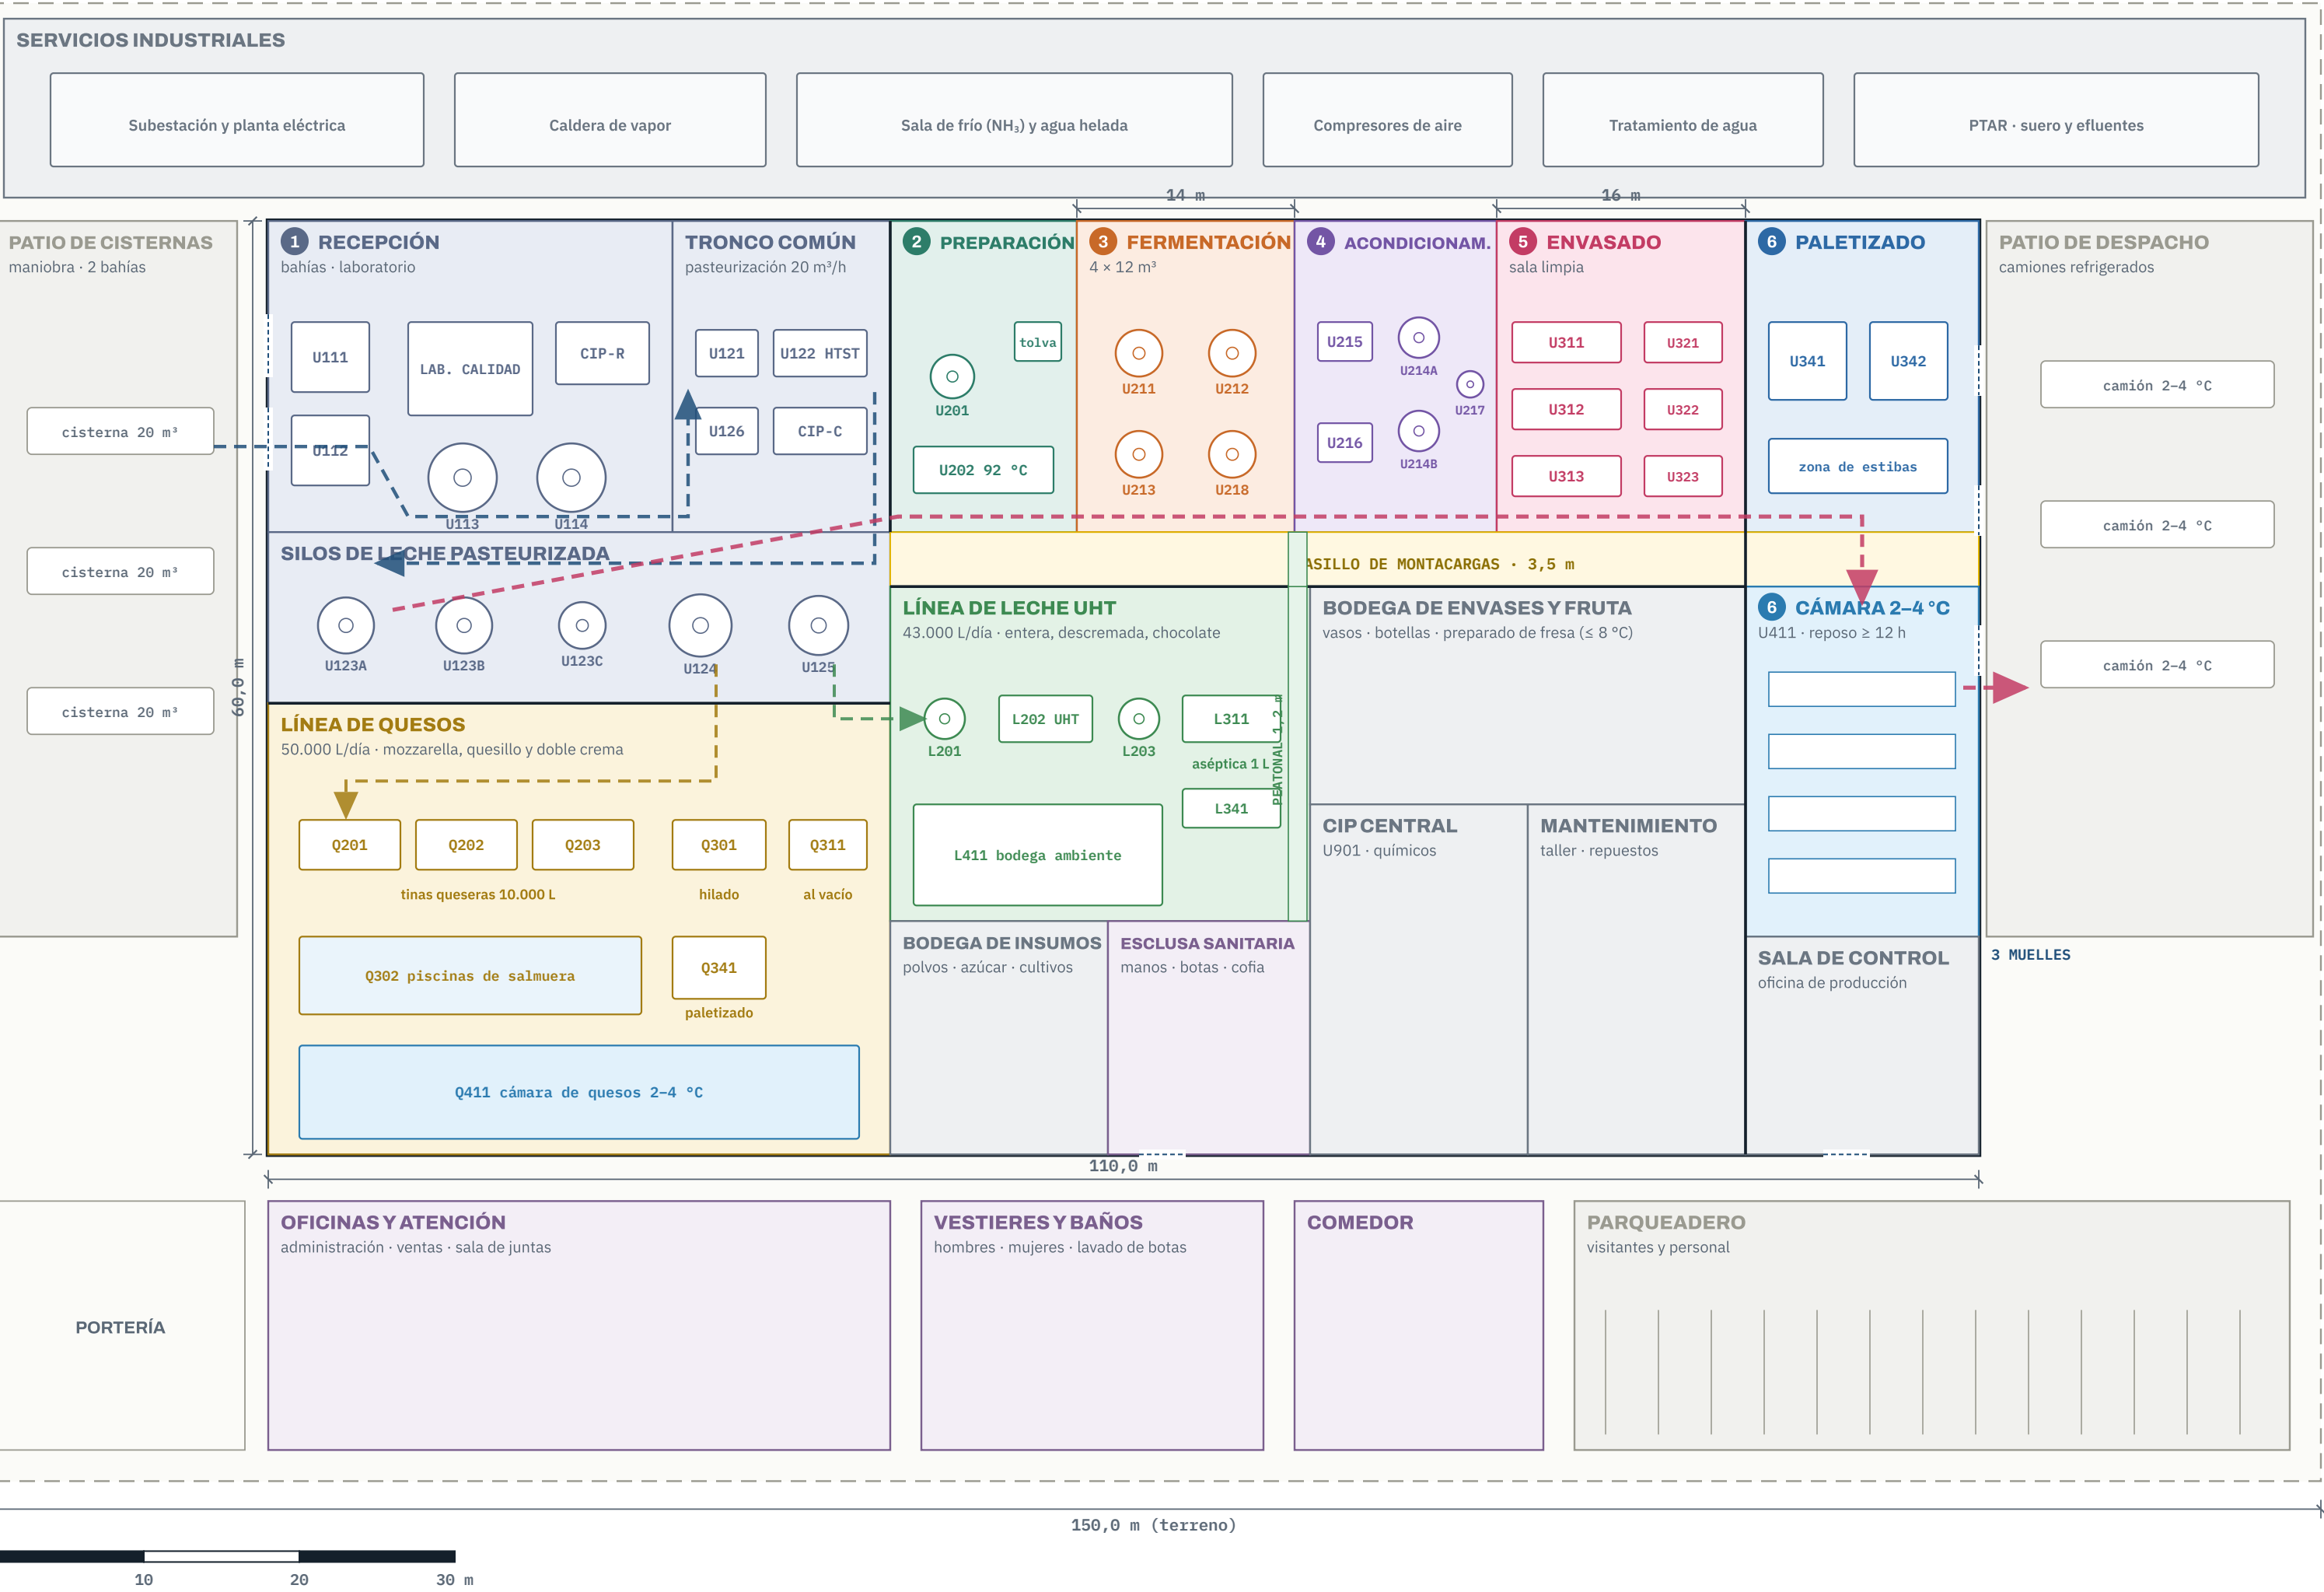

Convenciones

- Flujo del yogur (de la leche cruda al despacho)
- Flujo de leche cruda y pasteurizada
- Leche hacia quesos
- Leche hacia leche UHT
- Tanque o silo (código ISA-88)
- Equipo de proceso
- Pasillo de montacargas
- Sección de la línea (igual que en Tecnomatix)

Cuadro de áreas

|                                         |           |
|-----------------------------------------|-----------|
| Recepción, tronco común y silos         | 1.240 m²  |
| Línea de yogures                        | 1.400 m²  |
| Línea de quesos                         | 1.160 m²  |
| Línea de leche UHT                      | 580 m²    |
| Cámara de producto terminado            | 338 m²    |
| Bodegas, CIP, mantenimiento y servicios | 2.551 m²  |
| Personal, oficinas y esclusa            | 1.443 m²  |
| Patios, parqueadero y maniobra          | 2.415 m²  |
| Nave de producción                      | 6.600 m²  |
| Terreno                                 | 14.250 m² |

Criterios

Flujo en línea de oeste a este: lo crudo y lo terminado no se cruzan (BPM, Res. 2674/2013). Envasado en sala limpia, con acceso solo por la esclusa sanitaria. Fermentación junto a envasado para acortar tuberías de producto. Cámara junto a los muelles: el despacho no atraviesa producción. Servicios al norte, fuera de la nave. Medidas propuestas por Mekvra: se ajustan cuando haya plano del terreno.

PROYECTO  
Proyecto integrador APM 2026-2S • UNAL

PLANO  
Distribución en planta • tres líneas

ESCALA  
1:500 en A3 • metros

FECHA  
10-oct-2026

Mekvra • líder de instrumentación y software