


Lácteos Altos de Teusacá · planta de 150.000 L/día

Yogures ≈ 57.000 L/día (detalle) · quesos 50.000 L/día · leche UHT 43.000 L/día · flujo de oeste (recepción) a este (despacho)

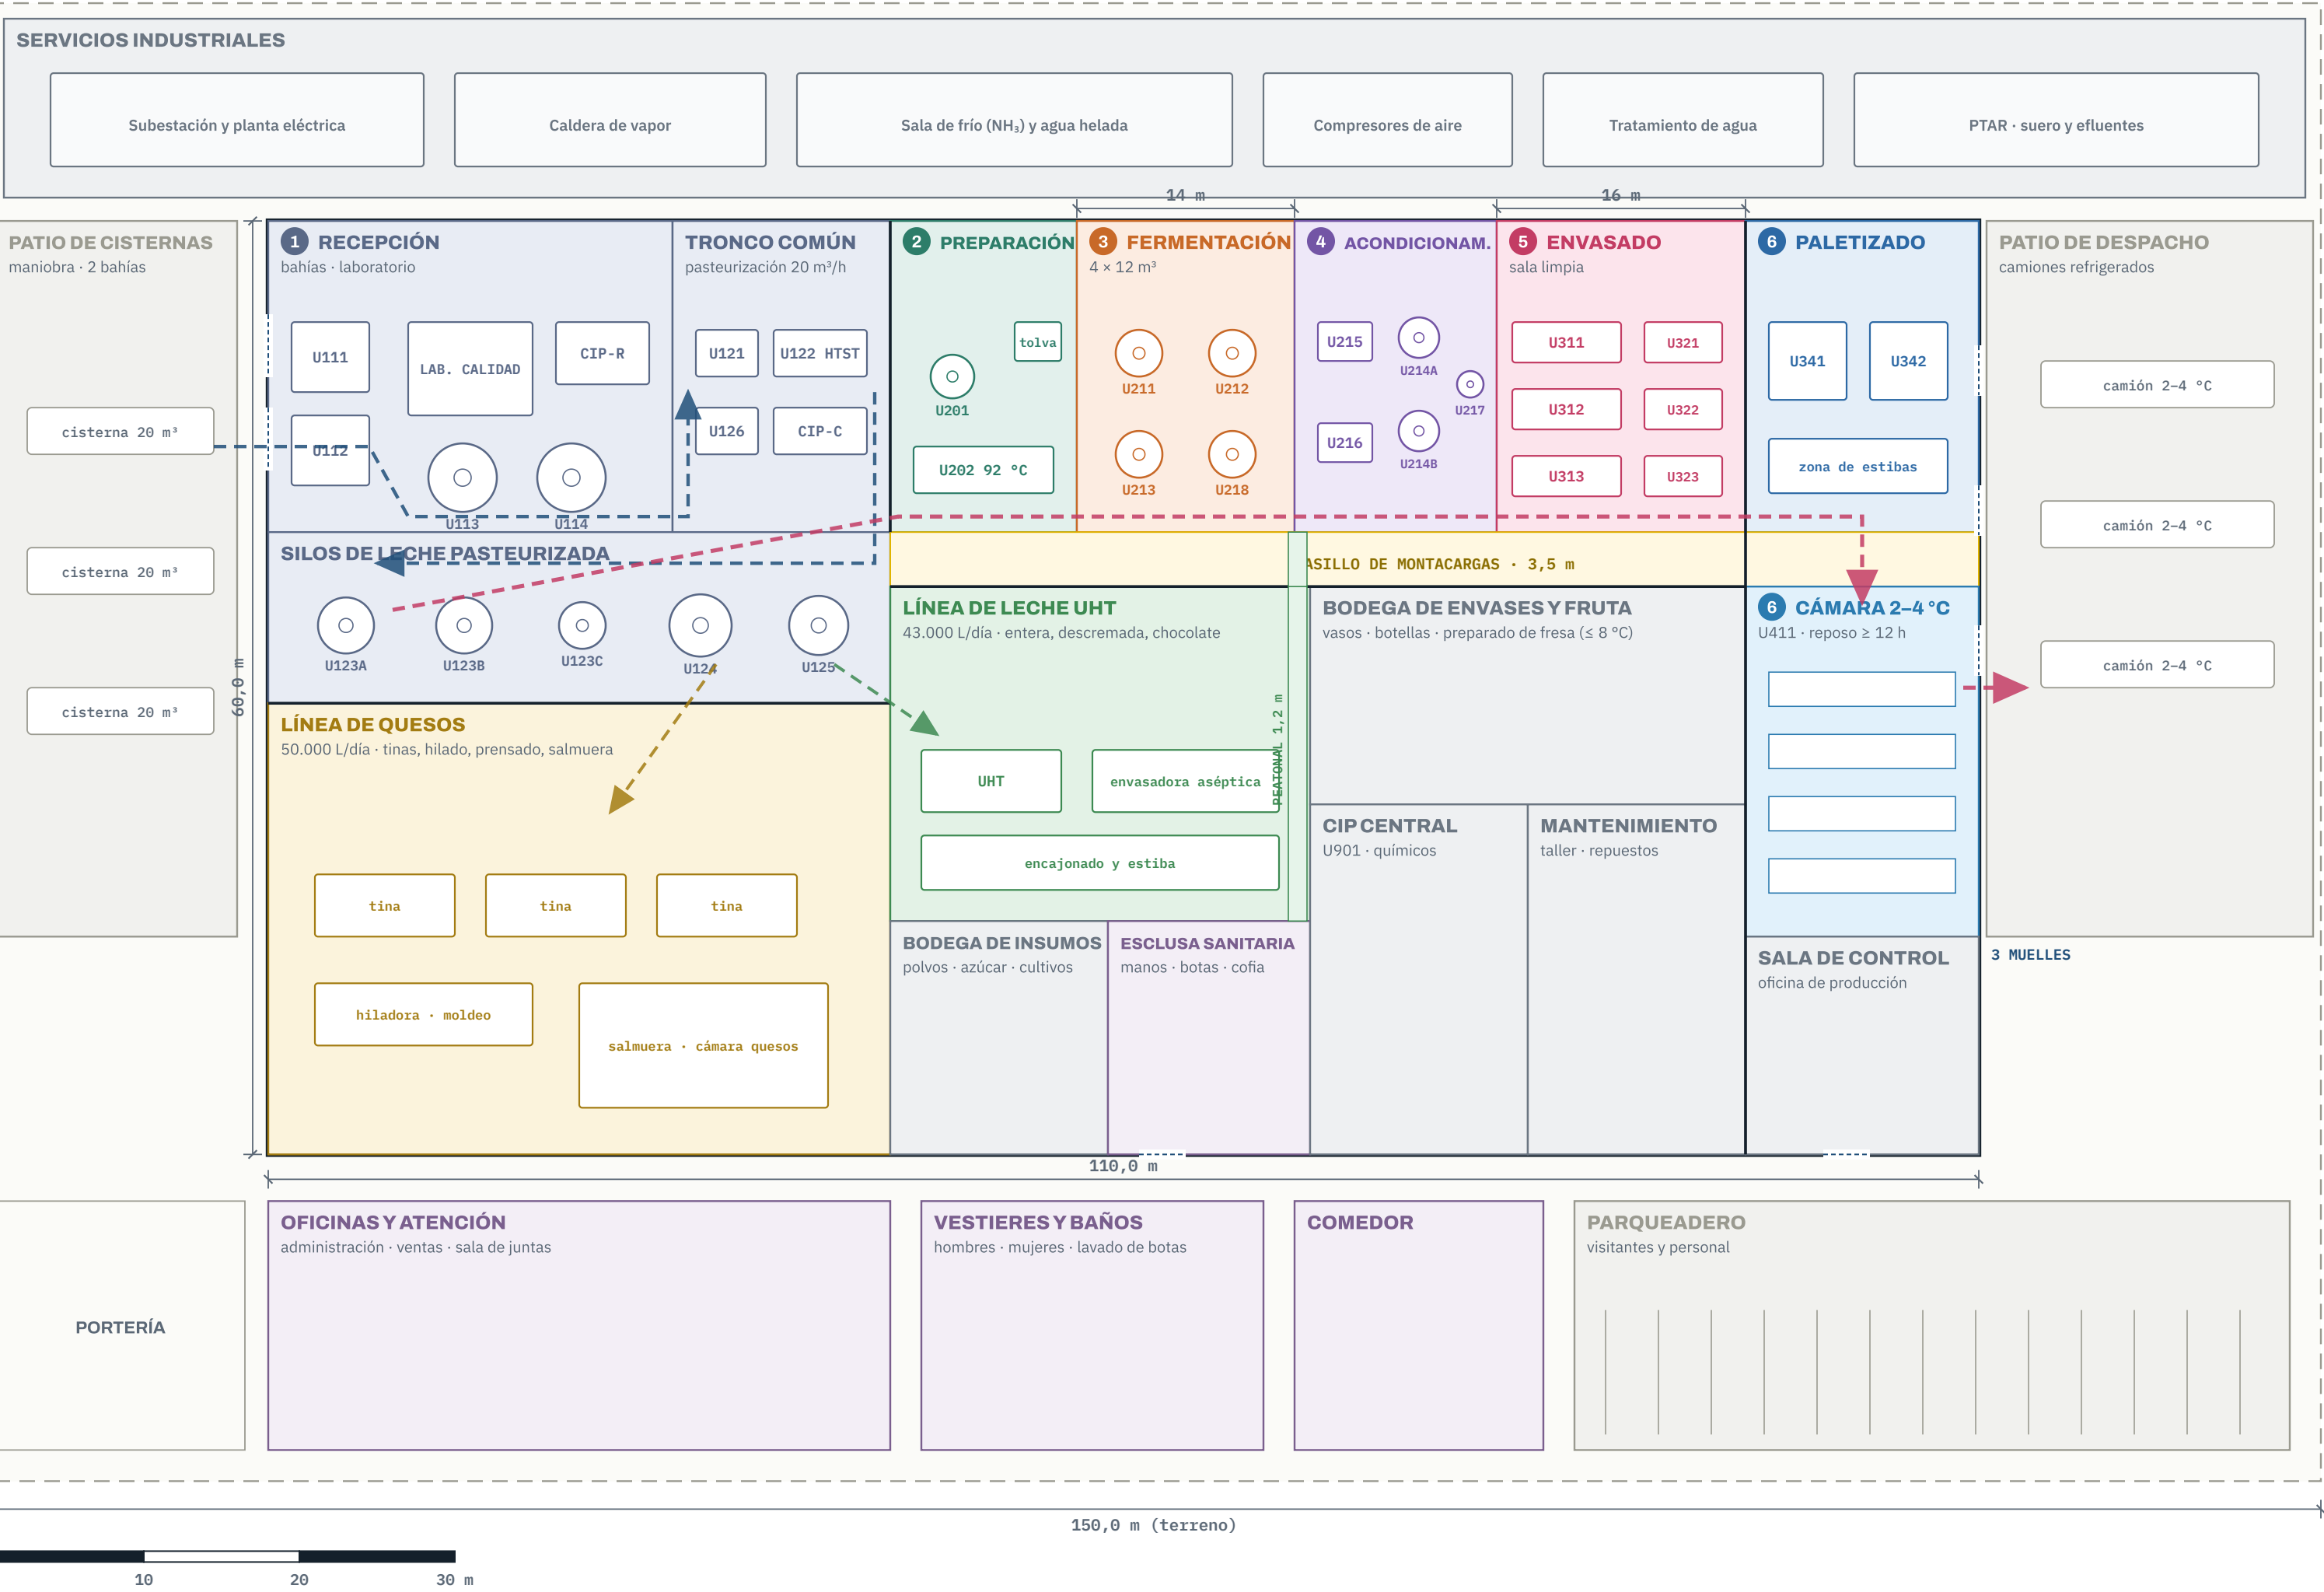

Convenciones

- Flujo del yogur (de la leche cruda al despacho)
- Flujo de leche cruda y pasteurizada
- Leche hacia quesos
- Leche hacia leche UHT
- Tanque o silo (código ISA-88)
- Equipo de proceso
- Pasillo de montacargas
- Sección de la línea (igual que en Tecnomatix)

Cuadro de áreas

Recepción, tronco común y silos	1.240 m²
Línea de yogures	1.400 m²
Línea de quesos	1.160 m²
Línea de leche UHT	580 m²
Cámara de producto terminado	338 m²
Bodegas, CIP, mantenimiento y servicios	2.551 m²
Personal, oficinas y esclusa	1.443 m²
Patios, parqueadero y maniobra	2.415 m²
Nave de producción	6.600 m²
Terreno	14.250 m²

Criterios

Flujo en línea de oeste a este: lo crudo y lo terminado no se cruzan (BPM, Res. 2674/2013).
Envasado en sala limpia, con acceso solo por la esclusa sanitaria.
Fermentación junto a envasado para acortar tuberías de producto.
Cámara junto a los muelles: el despacho no atraviesa producción.
Servicios al norte, fuera de la nave.
Medidas propuestas por Mekvra: se ajustan cuando haya plano del terreno.

PROYECTO
Proyecto integrador APM 2026-2S · UNAL

PLANO
Distribución en planta · estado actual

ESCALA
1:500 en A3 · metros

FECHA
10-oct-2026

Mekvra · líder de instrumentación y software